


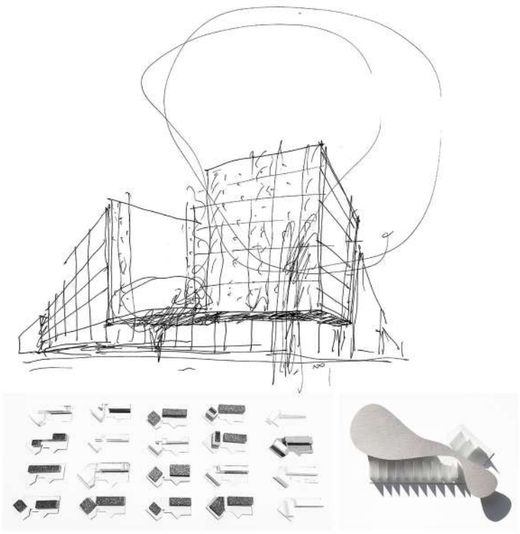


AKSONOMETRIČNI PRIKAZ VEČSTANOVANJSKEGA OBJEKTA

VEČSTANOVANJSKI OBJEKT DVOŘAKOVA

Vsekakor je nadvse dobrodošlo, da sta Mestna občina Maribor in Javni medobčinski stanovanjski sklad Maribor izbrala lokacijo za gradnjo najemnih stanovanj za mlade in mlade družine v neposredni bližini mestnega središča. Toliko bolj, ker se vsa večja mesta soočajo s pojavom gentrifikacije, ki izriva prebivalstvo s skromnejšimi dohodki na mestni rob. Obenem pa prav mladi zagotavljajo mestu vitalnost, kar je izjemno pomembno prav za območje Tabora, ki ima značaj delavskega predela in je dovolj gosto pozidan, a večinoma s stanovanjskimi objekti, zgrajenimi v šestdesetih letih preteklega stoletja. Večja skupnost mladih družin bo brez dvoma vnesla v prostor novo energijo, ki bo vplivala na življenjski utrip in značaj širšega območja.

Mladi in mlade družine živijo drugače kot starejši, zato so se v svetu že uveljavile tipologije stanovanjskih objektov, ki so prirejene novim načinom bivanja, aktivnejšemu preživljanju prostega časa, intenzivnejšemu druženju in medsebojni pomoči pri vsakodnevnih opravilih, varovanju otrok, gojenju vrtnin, deljenju skupnih prostorov, prevoznih sredstev, koles, avtomobilov ipd. Pri nas so tovrstni poskusi še skromni, je pa natečaj priložnost, da presežemo preživete stereotipe o gradnji neprofitnih najemniških stanovanj , kiimajo enako funkcionalno in prostorsko logiko kot luksuzna stanovanja, a bistveno manjše prostore.

Dobro stanovanje mora biti prostorno. Zato je temeljni problem socialne gradnje kako ustvariti večje bivalne prostore kljub skromnim kvadraturam. Kako kljub minimalnim dimenzijam prostorov zasnovati stanovanje, ki ne ustvarja neprijetnega občutka utesnjenosti, temveč prostosti. V tem smislu predlagamo tipologijo ***»odprtega tlorisa«***, ki ga odlikuje vtis prostornosti zaradi ***dvostranske orientacije***, ki se s pogledi širi na obe strani v ***zunanjost*** in ***zelenje.***

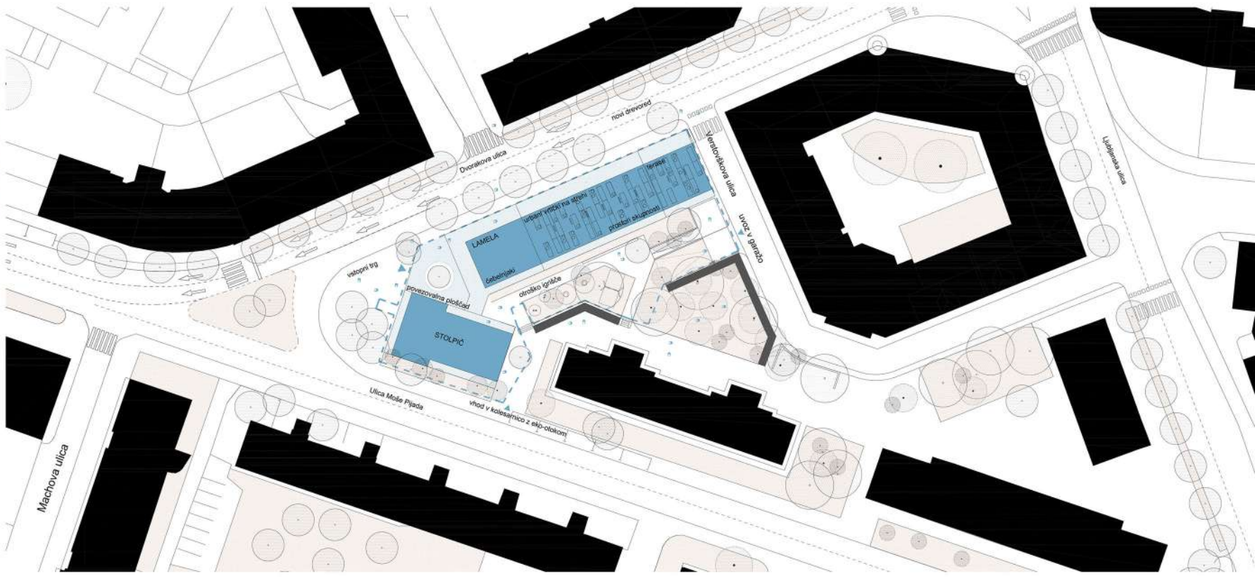


SITUACIJA , M_1:500


URBANISTIČNA ZASNOVA

Urbanistična zasnova sledi logiki robne zazidave kareja z ločenimi vzdolžnimi objekti, ki je značilna za območje med Dvořakovo ulico, ulico moše pijada in ljubljansko ulico. V tem smislu je predvidena novogradnja deljena na dva objekta, ki oblikujeta »odprt« zahodni vogal (analogno kot na vzhodni strani), z vmesnim prehodom (pokrito pasažo) v parkovno urejeno notranjost stanovanjskega območja.


OBRAVNAVANI PROSTOR

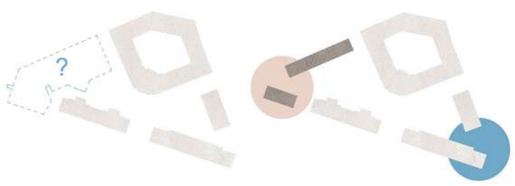


ANALOGIJA ODPRTEGA VOGALA

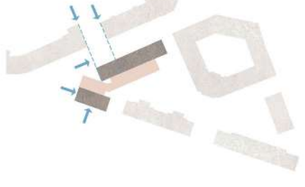

NAVEZOVANJE NA OBSTOJEČE OBJEKTE

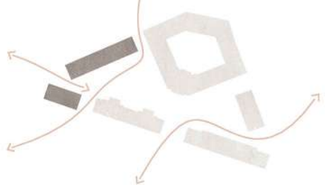


PREHAJANJE V PROSTORU MED OBJEKTI

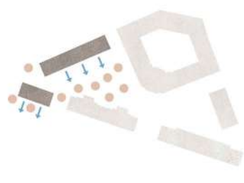

ORIENTACIJA STANOVANJ PROTI JUGU

TLORIS PRITLIČJA S SITUACIJO , M_1:500

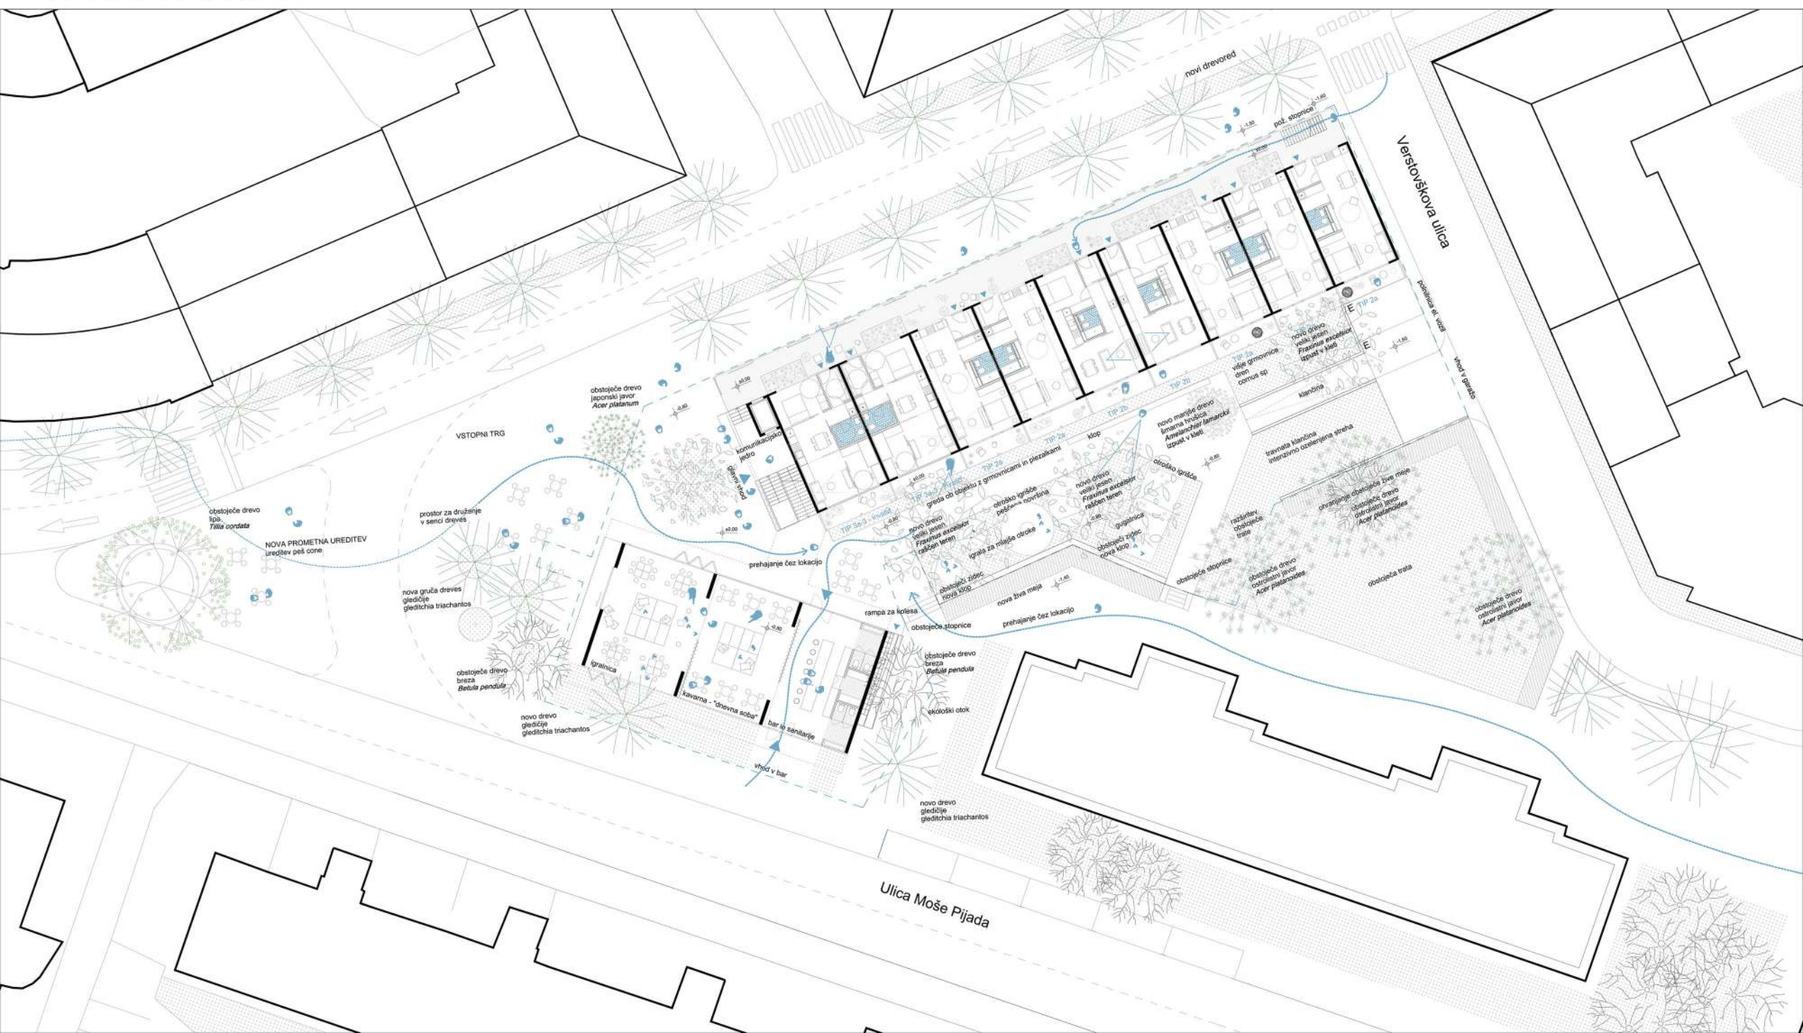


ARHITEKTURNA ZASNOVA

Vsa stanovanja so zato postavljena prečno in sežejo od ene fasade do druge, z ene strani so dodani ganki, z druge zasebni balkon. Dvostranska orientacija zagotavlja tudi najboljše prezračevanje in najboljšo osvetlitev ter osončenost. Poleg tega omogoča odprti tloris tudi bistveno večjo fleksibilnost in izrabo prostorov.

DVOSTRANSKO OSVETLJENO IN PREZRAČEVANO STANOVANJE

Vsa stanovanja so zato postavljena prečno in sežejo od ene fasade do druge, z ene strani so dodani ganki, z druge zasebni balkon. Dvostranska orientacija zagotavlja tudi najboljše prezračevanje in najboljšo osvetlitev ter osončenost. Poleg tega omogoča odprti tloris tudi bistveno večjo fleksibilnost in izrabo prostorov.

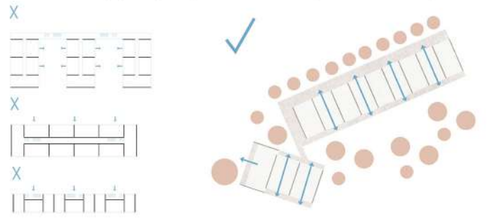


ENOSTRANSKO ORIENTIRANO STANOVANJE

- neustrezen odnos med velikostjo dnevnih in nočnih prostorov
- enostranska osvetljenost in prezračevanje prostorov
- neprilagodljivost tlorisnih zasnov


DVOSTRANSKO OSVETLJENO IN PREZRAČEVANO STANOVANJE

+ popolna fleksibilnost
+ obojestransko osvetljeno stanovanje
+ obojestransko prezračevano stanovanje
+ ustrezna velikost med dnevnimi in spalnimi prostori

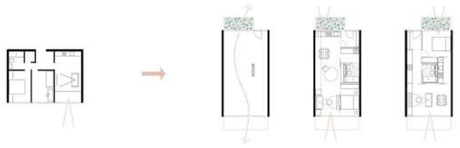

FLEKSIBILNOST STANOVANJ

Popolna notranja fleksibilnost stanovanj, z možnostjo rotacije prefabriciranega sanitarnega jedra okoli vertikalnih instalacij, kar omogoča krožno ali linijsko organizacijo stanovanja.

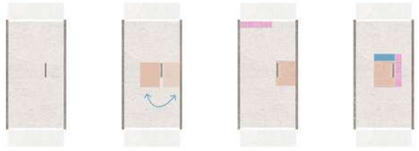

Prikaz prilagoditve stanovanja glede na strukturo stanovalcev oz. spreminjanja skozi čas:



ZELENA BARIERA


Novi drevored izboljšuje bivalne pogoje okoliškim stanovalcem Dvorakove ulice in blaži hrupnost,ki jo povzroča promet. Stanovalci do stanovanjskih enot prehajajo med vertikalno zeleno režo in drevoredom, ki zagotavlja intimnost stanovanjskim prostorom in kvalitetno vpliva na skupne prostore druženja v objektu.




SKUPNI PROSTORI



V primeru nadgradnje se poveča tudi količina in raznolikost prostorov za skupnost.

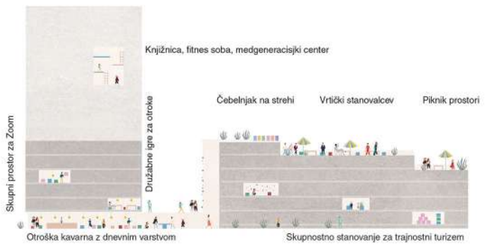

KONSTRUKCIJSKA SHEMA

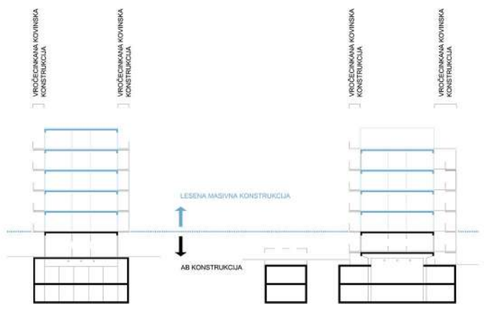


PREČNI PREREZ UL. MOŠE PIJADE

PREČNI PREREZ DVORAKOVA ULICA


TLORIS PRVE KLETI

M_1:200

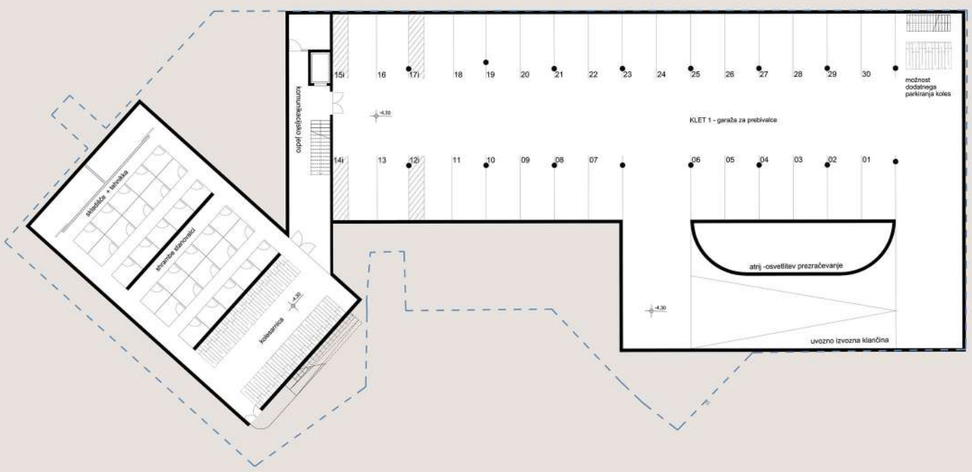


TLORIS DRUGE KLETI

M_1:200

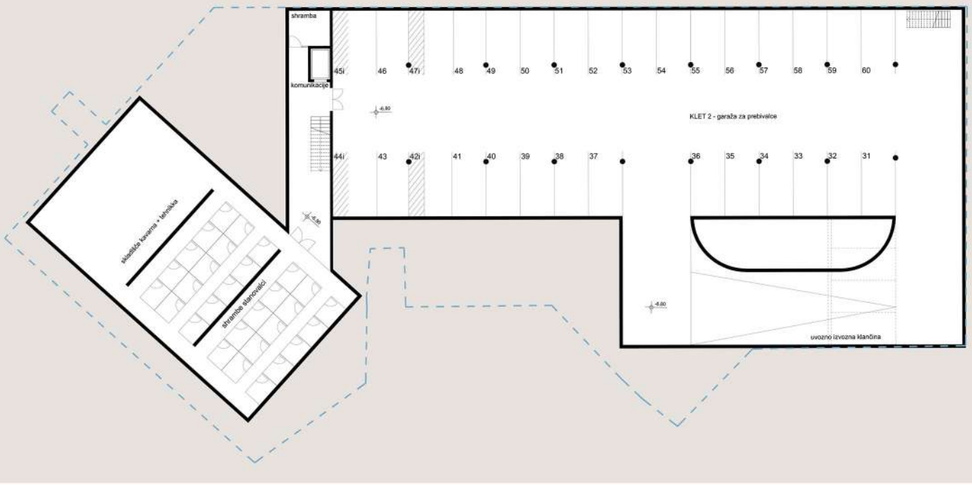



MOŽNOST IZGRADNJE TRETJE KLETI

M_1:200

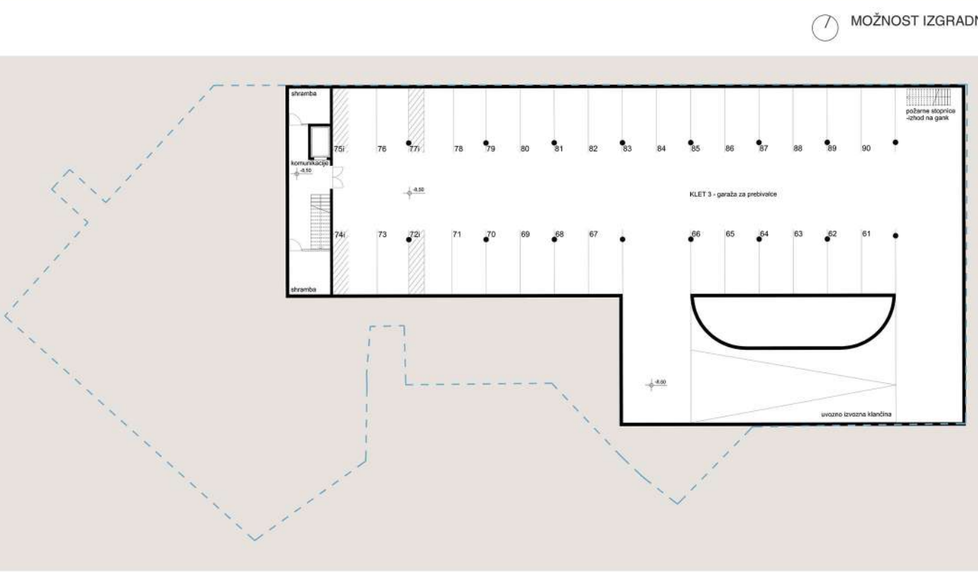

ENAKO KOT SO STANOVANJA POMEMBNA ZA KVALITETO DRUŽINSKEGA ŽIVLJENJA, SO TUDI SKUPNI PROSTORI POMEMBNI ZA VSAKODNEVNO ŽIVLJENJE SKUPNOSTI. TO SO RAZŠIRJENI HODNIKI / GANKI PRED STANOVANJI, KI SO PRILOŽNOST ZA NAKLJUČNA SREČANJA IN IGRO OTROK, RAVNE STREHE Z DVIGNJENIMI GREDAMI ZA DRUŽENJE OB GOJENJU VRTNIN, TERASA NAD PASAŽO MED OBJEKTOMA ZA RAZNE PRIREDITVE NA PROSTEM, IGRALA ZA OTROKE NA JUŽNI STRANI STANOVANJSKEGA OBJEKTA, MANJŠI GOSTINSKI LOKAL S TERASO NA KRIŽIŠČU, KI MU JE PRIKLJUČEN SKUPNI PROSTOR ZA NAJRAZLIČNEJŠE DEJAVNOSTI, DRUŽENJA, PRAZNOVANJA, SESTANKE IN IGRO OTROK V OBDOBJIH, KO NI MOŽNO ZADRŽEVANJE NA PROSTEM.

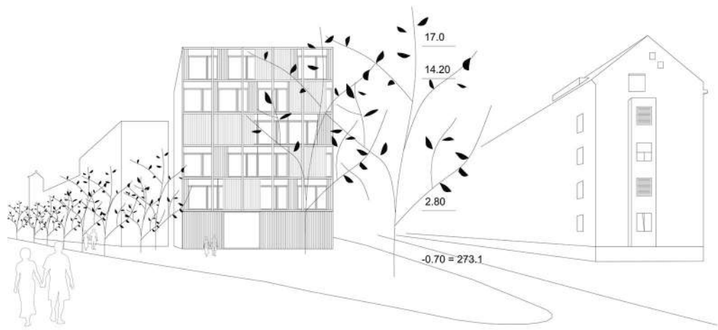

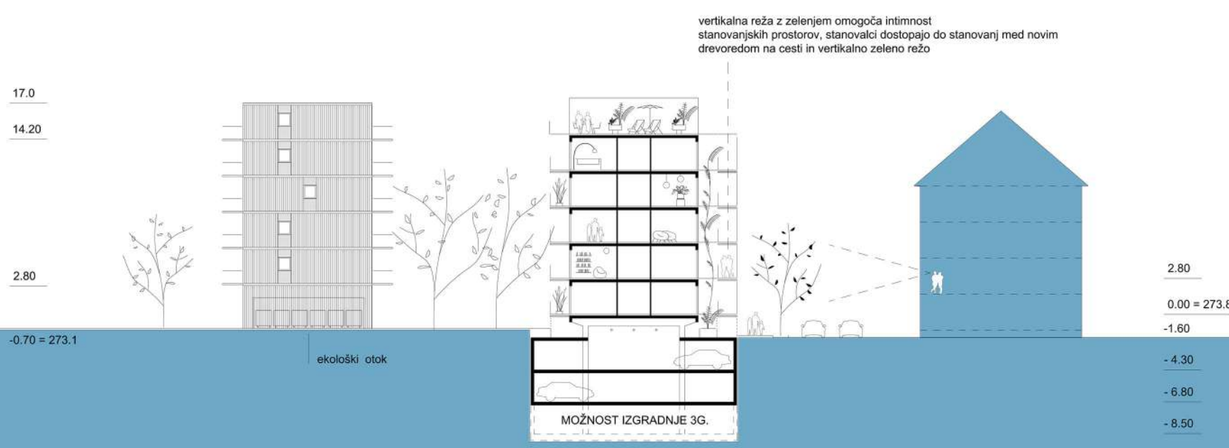



POGLED NA VHODNO PLOŠČAD


KATALOG STANOVANJ
M_ 1:100




rekapitulacija	TIP 1	TIP 2	TIP 3	TIP 4	TIP 5	SKUPAJ
	6 enot	21 enot	18 enot	10 enot	5 enot	60 enot

TIP 1 + TIP 3

1a + 3b-1

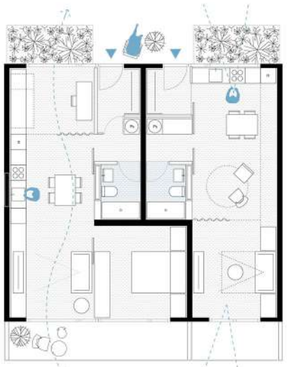


1b + 3b-2

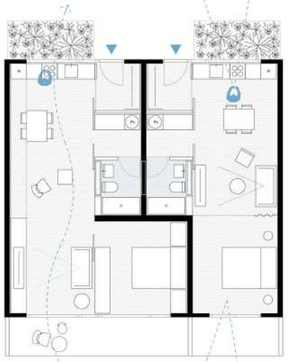


1c + 3b-3




TLORIS PRVEGA NADSTROPJA
M_1:200

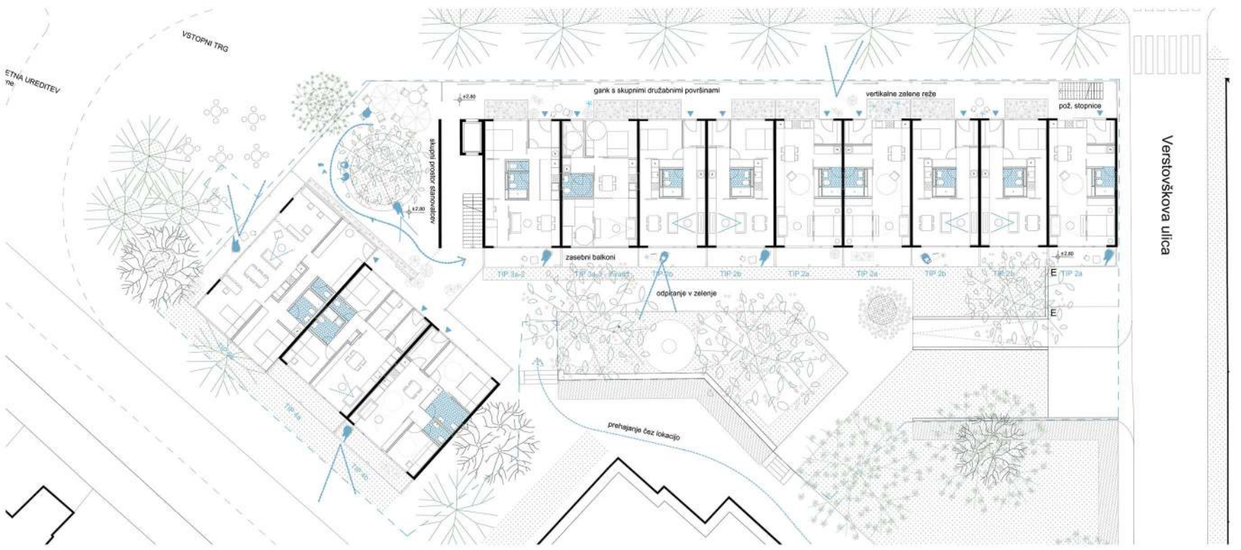

TLORIS DRUGEGA NADSTROPJA
M_1:200

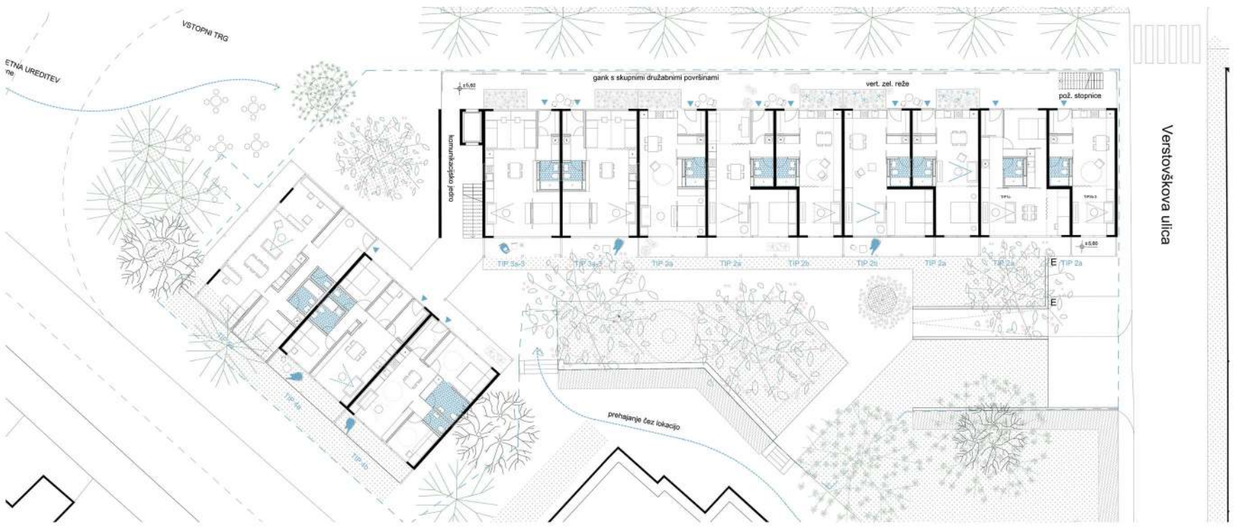


PREREZ A-A, M_1:200

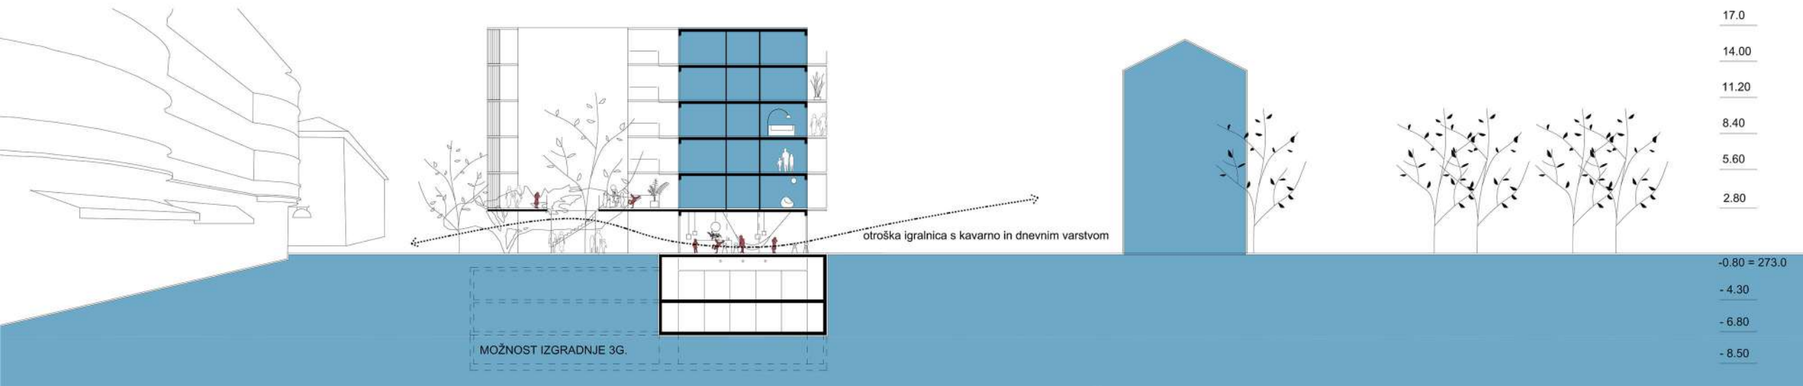

KATALOG STANOVANJ
M_1:100

TIP 2

2a

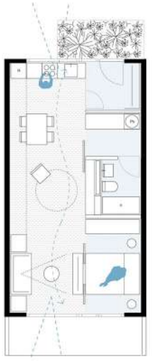

2b




TIP 3

3a-1



3a-2

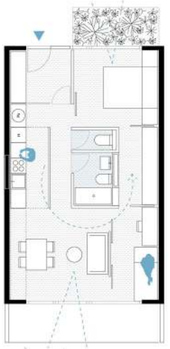

3a-3



3a-4
gibalno
ovirani



TIP 4

4a



4b




4c




TIP 5


5

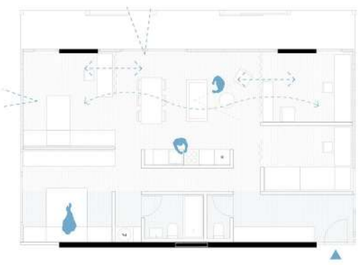


TLORIS TRETJEGA NADSTROPJA
M_1:200

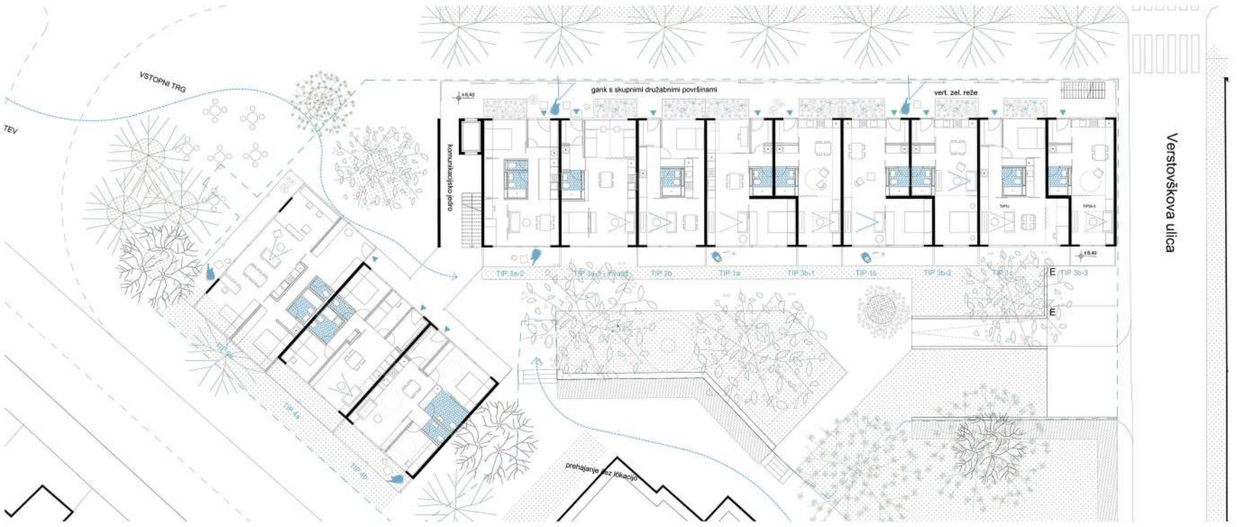

TLORIS ČETRTGA NADSTROPJA
M_1:200

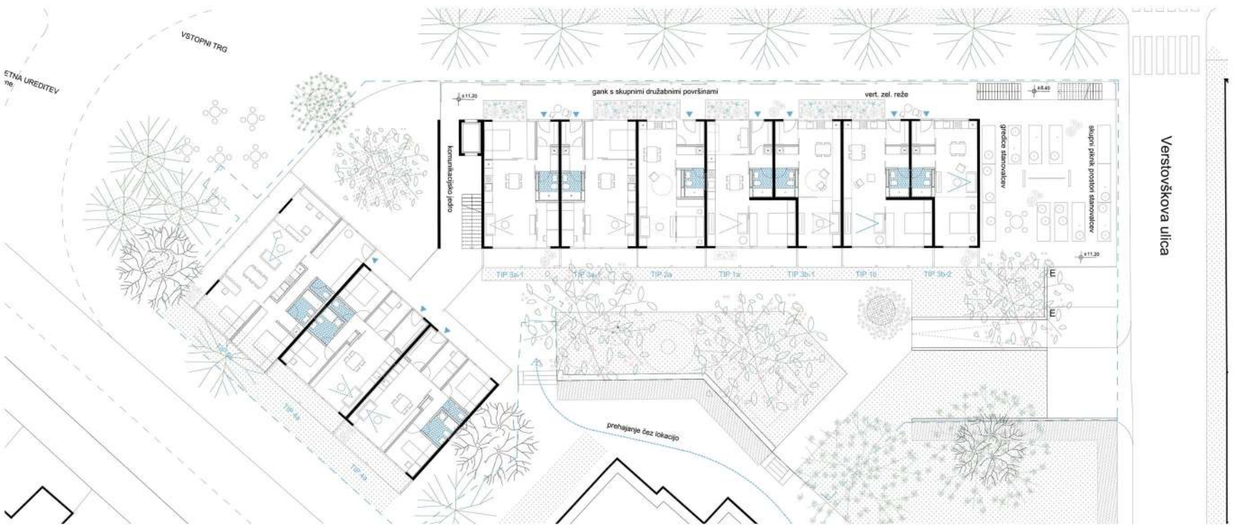


TLORIS PETEGA NADSTROPJA
M_1:200

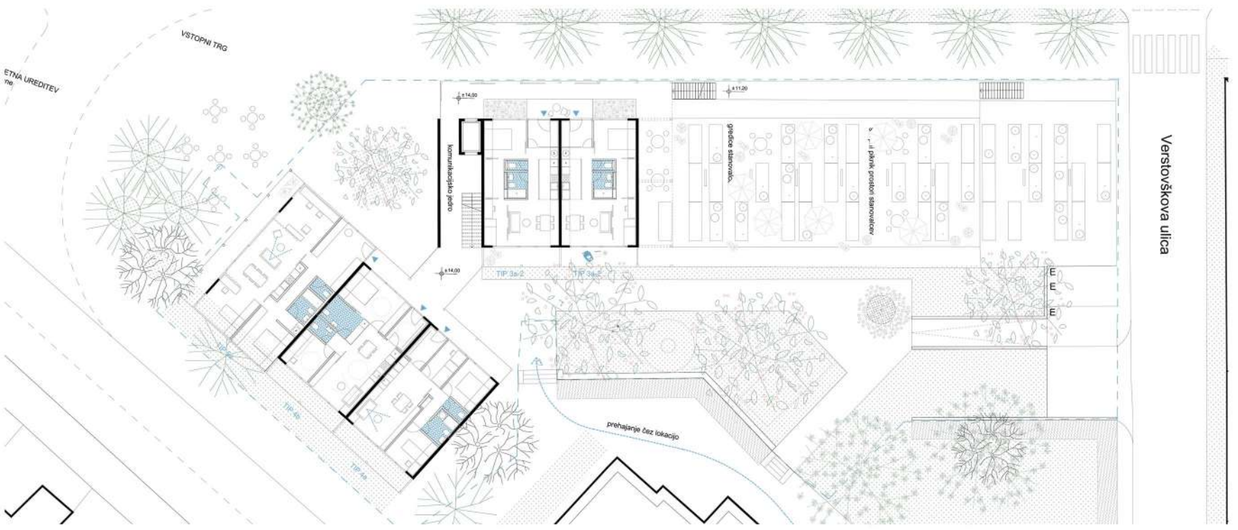

DOBRO STANOVANJE MORA BITI PROSTORNO. ZATO JE TEMELJNI PROBLEM SOCIALNE GRADNJE KAKO USTVARITI VEČJE BIVALNE PROSTORE KLJUB SKROMNIM KVADRATURAM. KAKO KLJUB MINIMALNIM DIMENZIJAM PROSTOROV ZASNOVATI STANOVANJE, KI NE USTVARJA NEPRIJETNEGA OBČUTKA UTESNJENOSTI, TEMVEČ PROSTOSTI. V TEM SMISLU PREDLAGAMO TIPOLOGIJO »ODPRTEGA TLORISA«, KI GA ODLIKUJE VTIS PROSTORNOSTI ZARADI DVOSTRANSKE ORIENTACIJE, KI SE S POGLEDI ŠIRI NA OBE STRANI V ZUNANJOST IN ZELENJE.

PREREZ B-B
M_1:200

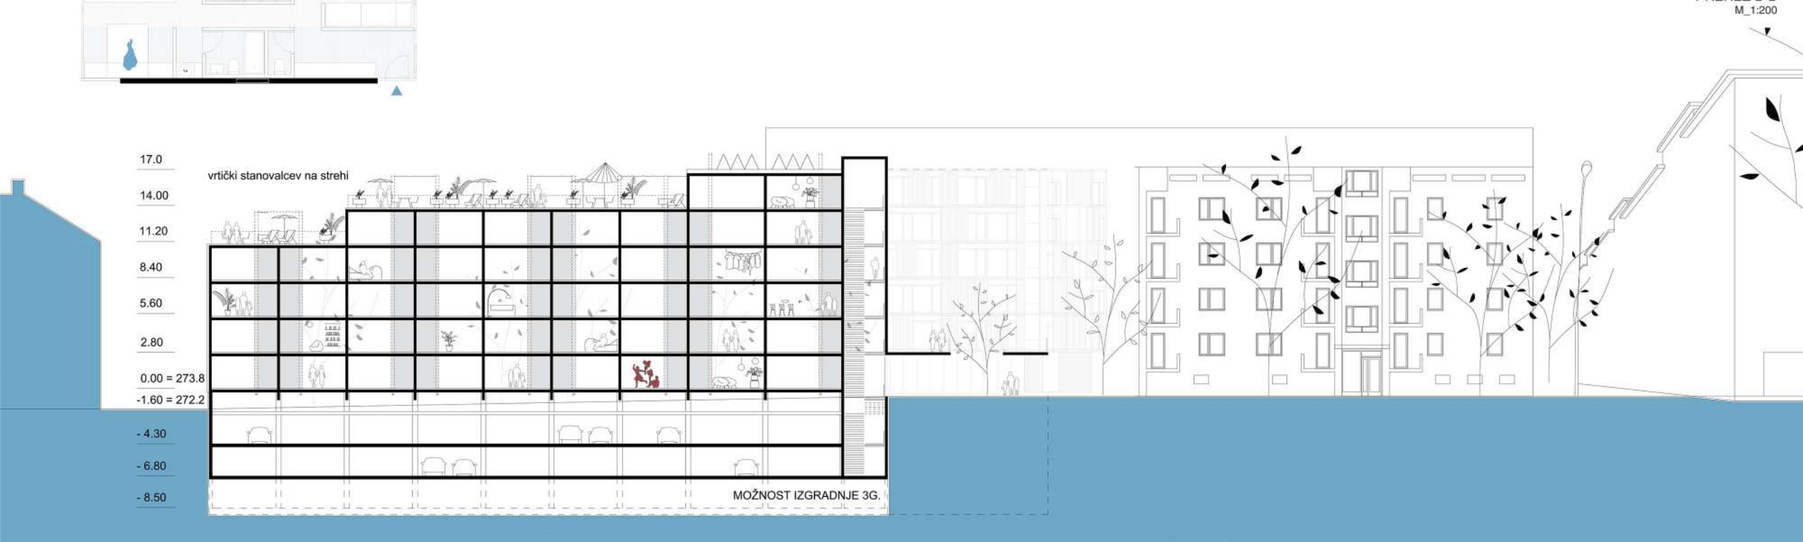




POGLED NA

PREČNO POSTAVLJENA STANOVANJA SO DOSTOPNA PREKO ZUNANJEGA HODNIKA - GANKA, KI JE TUDI PROSTOR SREČEVANJ IN NAKLJUČNEGA DRUŽENJA STANOVALCEV. TO POMENI TUDI ZNATNO RACIONALIZACIJO SKUPNIH PROSTOROV (ŠTEVILA STOPNIŠČ IN DVIGAL), KI SO PRISLONJENI K STAVBI. NA TA NAČIN SO ZNOTRAJ KOMPAKTNEGA FASADNEGA OVOJA ZGOLJ STANOVANJA, KAR JE TUDI ENERGETSKO IZJEMNO VARČNO.

SEVERNA FASADA
M_1:200




JUŽNA FASADA
M_1:200

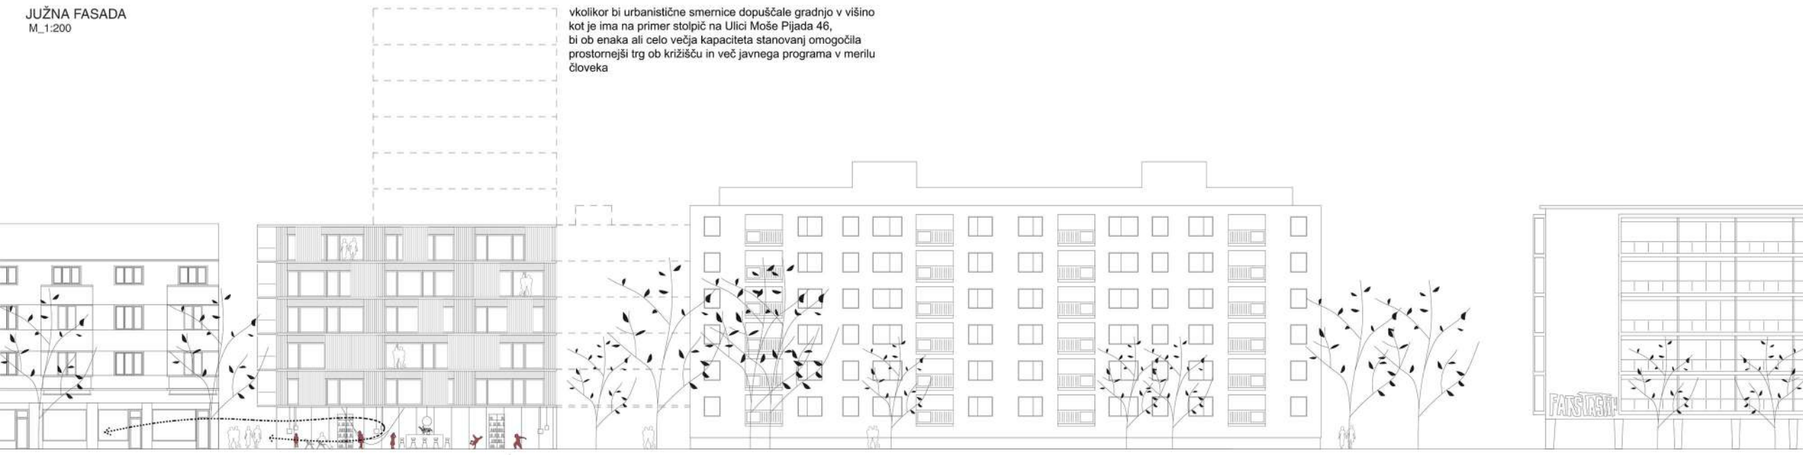

otroška igralnica s kavarno in dnevnim varstvom, ki
se odpira na zahodni trg in na zunanjo zeleno igrišče

PREČNI PREREZ (1-1)
M_1:200

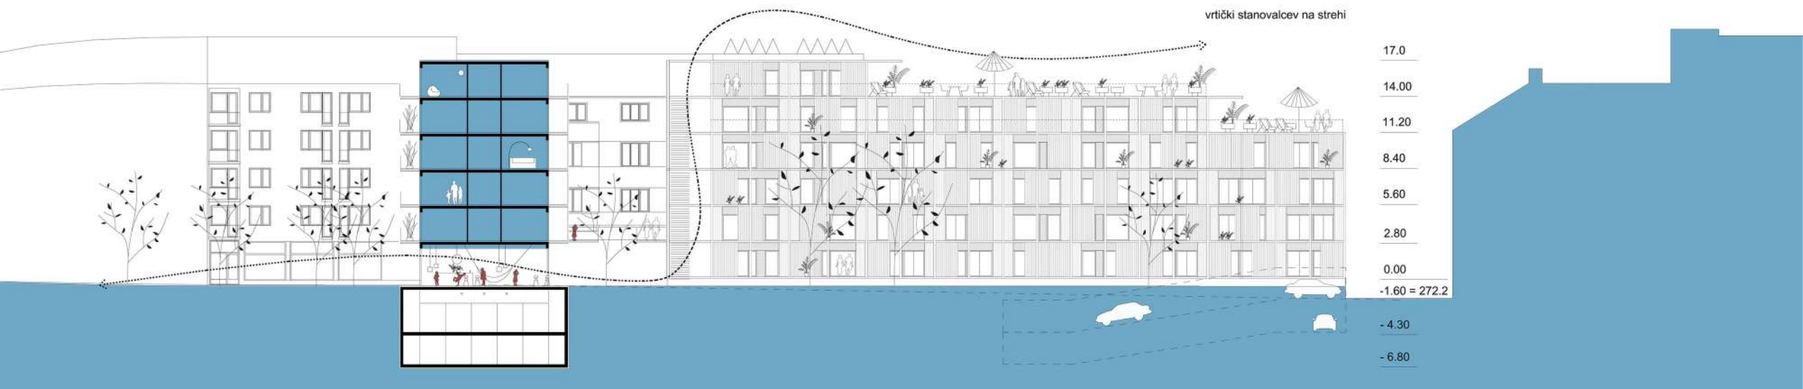

STANOVANJSKI BLOK (STANOVANJA ZA MLADE IN MLADE DRUŽINE)
DVORAKOVA ULICA (MARIBOR)

Številka nadstropja	Po potrebi vstavite dodatne prazne vrstice, jih preimenujte (drugi načrtovani funkcionalni prostori) ali izbrišite prazne vrstice (potrebna je kontrola formul). V pritličju navedite načrtovane funkcionalne prostore (npr. kolesarnica, vhodna avla itd.) V garaži navedite tudi načrtovane funkcionalne prostore.	Tip stanovanja (v kolikor gre za drug funkcionalni prostor, pustite prazno)	NETO* TLORISNA POVRŠINA STANOVANJA [m2]	NETO* TLORISNA POVRŠINA BALKONA / LOŽE [m2]	NETO* TLORISNA POVRŠINA SHRAMBE IZVEN STANOVANJA [m2]	NETO* TLORISNA POVRŠINA SKUPNIH PROSTOROV [m2]	SKUPNA NETO TLORISNA POVRŠINA TEHNIČNIH POVRŠIN [m2]	SKUPNA NETO TLORISNA POVRŠINA KOMUNIKACIJ [m2]	NETO TLORISNA POVRŠINA NADSTROPJA (NTP) [m2] (I+K+L+M+N)	BRUTO TLORISNA POVRŠINA NADSTROPJA (BTP) [m2]
5	Stanovanje 1	Tip 3	57,10	10,30	3,00	Streha z vrtički in pros				
	Stanovanje 2	Tip 3	57,10	10,30	3,00					
	Stanovanje 3	Tip 4	67,20	10,00	3,00					
	Stanovanje 4	Tip 4	67,20	10,00	3,00					
	Stanovanje 5	Tip 5	94,00	13,00	3,00					
	Stanovanje 6									
	Stanovanje 7									
	Stanovanje 8									
	Stanovanje 9									
	Sranovanje 10									
	Stanovanje 11									
	Stanovanje 12									
	"Drugi funkcionalni prostor"									
	"Drugi funkcionalni prostor"									
	"Drugi funkcionalni prostor"									
Skupaj (5. nadstropje):			**342,60**	**53,60**	**15,00**	**260,00**	**7,20**	**75,00**	**699,80**	**771,00**
4	Stanovanje 1	Tip 1	41,90	4,90	3,00					
	Stanovanje 2	Tip 3	57,10	10,30	3,00					
	Stanovanje 3	Tip 1	41,90	4,90	3,00					
	Stanovanje 4	Tip 3	57,10	10,30	3,00					
	Stanovanje 5	TIP 2	48,90	7,65	3,00					
	Stanovanje 6	TIP 3	57,10	8,71	3,00					
	Stanovanje 7	TIP 3	57,10	8,71	3,00					
	Stanovanje 8	Tip 4	67,20	10,00	3,00	Streha z vrtički in pros				
	Stanovanje 9	Tip 4	67,20	10,00	3,00					
	Stanovanje 10	Tip 5	94,00	13,00	3,00					
	Stanovanje 11									
	Stanovanje 12									
	"Drugi funkcionalni prostor"									
	"Drugi funkcionalni prostor"									
	"Drugi funkcionalni prostor"									
Skupaj (4. nadstropje):			**589,50**	**88,47**	**30,00**	**115,00**	**8,40**	**135,00**	**877,90**	**878,20**
3	Stanovanje 1	Tip 1	41,90	4,90	3,00					
	Stanovanje 2	Tip 3	57,10	10,30	3,00					
	Stanovanje 3	Tip 1	41,90	4,90	3,00					
	Stanovanje 4	Tip 3	57,10	10,30	3,00					
	Stanovanje 5	Tip 1	41,90	4,90	3,00					
	Stanovanje 6	Tip 3	57,10	10,30	3,00					
	Stanovanje 7	TIP 2	48,90	7,65	3,00					
	Stanovanje 8	TIP 3	57,10	8,71	3,00	Razširitvene površine r				
	Stanovanje 9	TIP 3	57,10	8,71	3,00					
	Stanovanje 10	Tip 4i	67,20	10,00	3,00					
	Stanovanje 11	Tip 4	67,20	10,00	3,00					
	Stanovanje 12	Tip 5	94,00	13,00	3,00					
	"Drugi funkcionalni prostor"									
	"Drugi funkcionalni prostor"									
	"Drugi funkcionalni prostor"									
Skupaj (3. nadstropje):			**688,50**	**103,67**	**36,00**	**15,00**	**9,00**	**135,00**	**883,50**	**1.015,20**

2	Stanovanje 1	Tip 1	41,90	4,90	3,00					
	Stanovanje 2	Tip 3	57,10	10,30	3,00					
	Stanovanje 3	TIP 2	48,90	7,65	3,00					
	Stanovanje 4	TIP 2	48,90	7,65	3,00					
	Stanovanje 5	TIP 2	48,90	7,65	3,00					
	Stanovanje 6	TIP 2	48,90	7,65	3,00					
	Stanovanje 7	TIP 2	48,90	7,65	3,00					
	Stanovanje 8	TIP 3	57,10	8,71	3,00	Razširitvene površine r				
	Stanovanje 9	TIP 3	57,10	8,71	3,00					
	Stanovanje 10	Tip 4i	67,20	10,00	3,00					
	Stanovanje 11	Tip 4	67,20	10,00	3,00					
	Stanovanje 12	Tip 5	94,00	13,00	3,00					
	"Drugi funkcionalni prostor"									
	"Drugi funkcionalni prostor"									
	"Drugi funkcionalni prostor"									
Skupaj (2. nadstropje):			**686,10**	**103,87**	**36,00**	**15,00**	**9,00**	**135,00**	**881,10**	**1.015,20**
1	Stanovanje 1	TIP 2	48,90	7,65	3,00					
	Stanovanje 2	TIP 2	48,90	7,65	3,00					
	Stanovanje 3	TIP 2	48,90	7,65	3,00					
	Stanovanje 4	TIP 2	48,90	7,65	3,00					
	Stanovanje 5	TIP 2	48,90	7,65	3,00					
	Stanovanje 6	TIP 2	48,90	7,65	3,00					
	Stanovanje 7	TIP 2	48,90	7,65	3,00					
	Stanovanje 8	TIP 3i	57,10	8,71	3,00	Razširitvene površine r				
	Stanovanje 9	TIP 3	57,10	8,71	3,00					
	Stanovanje 10	Tip 4	67,20	10,00	3,00					
	Stanovanje 11	Tip 4i	67,20	10,00	3,00					
	Stanovanje 12	Tip 5	94,00	13,00	3,00					
	"Drugi funkcionalni prostor"									
	"Drugi funkcionalni prostor"									
	"Drugi funkcionalni prostor"									
Skupaj (1. nadstropje):			**684,90**	**103,97**	**36,00**	**30,00**	**9,00**	**135,00**	**894,90**	**1.015,20**
P	Stanovanje 1	TIP 2	48,90	7,65	3,00					
	Stanovanje 2	TIP 2	48,90	7,65	3,00					
	Stanovanje 3	TIP 2	48,90	7,65	3,00					
	Stanovanje 4	TIP 2	48,90	7,65	3,00					
	Stanovanje 5	TIP 2	48,90	7,65	3,00					
	Stanovanje 6	TIP 2	48,90	7,65	3,00					
	Stanovanje 7	TIP 2	48,90	7,65	3,00					
	Stanovanje 8	Tip 3i	57,10	8,71	3,00	Otroška kavarna z vars				
	Stanovanje 9	TIP 3i	57,10	8,71	3,00					
	Otroška kavarna z varstvom		229,10							
	"Drugi funkcionalni prostor"									
	"Drugi funkcionalni prostor"									
	"Drugi funkcionalni prostor"									
Skupaj (pritličje):			**685,60**	**70,97**	**27,00**	**229,00**	**8,10**	**118,00**	**1.067,70**	**1.102,00**
Skupaj:			**3.677,20**	**524,55**	**180,00**	**664,00**	**50,70**	**733,00**	**5.304,90**	**5.796,80**

Garaža	Etaža	Število parkirnih mest	NETO* TLORISNA POVRŠINA PARKIRNIH MEST [m2]	NETO* TLORISNA POVRŠINA SHRAMBE IZVEN STANOVANJA [m2]	NETO* TLORISNA POVRŠINA SKUPNIH PROSTOROV [m2]	SKUPNA NETO TLORISNA POVRŠINA TEHNIČNIH POVRŠIN [m2]	SKUPNA NETO TLORISNA POVRŠINA KOMUNIKACIJ [m2]	NETO TLORISNA POVRŠINA GARAŽE (NTP) [m2] (I+J+K+L+M)	BRUTO TLORISNA POVRŠINA GARAŽE (BTP) [m2]	
garaža	**-1**	30	410,00	132,00	97,90	10,30	685,00	1.335,20	1.403,00	
garaža	**-2**	34	463,00	132,00	97,90	10,30	689,00	1.392,20	1.403,00	
garaža 3 (opcija)	**-3**	30								
Garaža skupaj:		**64**	**873,00**	**264,00**	**195,80**	**20,60**	**1.374,00**	**2.727,40**	**2.806,00**	

	NETO TLORISNA POVRŠINA (NTP) [m2]	BRUTO TLORISNA POVRŠINA (BTP) [m2]
SKUPAJ (nadzemni del)	**5.304,90**	**5.796,80**
SKUPAJ (podzemni del)	**2.727,40**	**2.806,00**
SKUPAJ:	**8.032,30**	**8.602,80**

Opomba:
- površine morajo biti izračunane skladno s SIST ISO 9836

Struktura stanovanj	Število stanovanj po tipih	Odstotek
Tip 1	**6,00**	**10,00**
Tip 2	**21,00**	**35**
Tip 3	**15,00**	**25**
Tip 3i	**3,00**	**5**
Tip 4	**7,00**	**11,66666667**
Tip 4i	**3,00**	**5**
Tip 5	**5,00**	**8,333333333**
Skupaj	**60,00**	**100,00**